


工	艺	专	业	审	核	日	期	
设	计	专	业	审	核	日	期	
建	筑	专	业	审	核	日	期	
图	纸	专	业	审	核	日	期	
电	气	专	业	审	核	日	期	
给	排	水	专	业	审	核	日	期

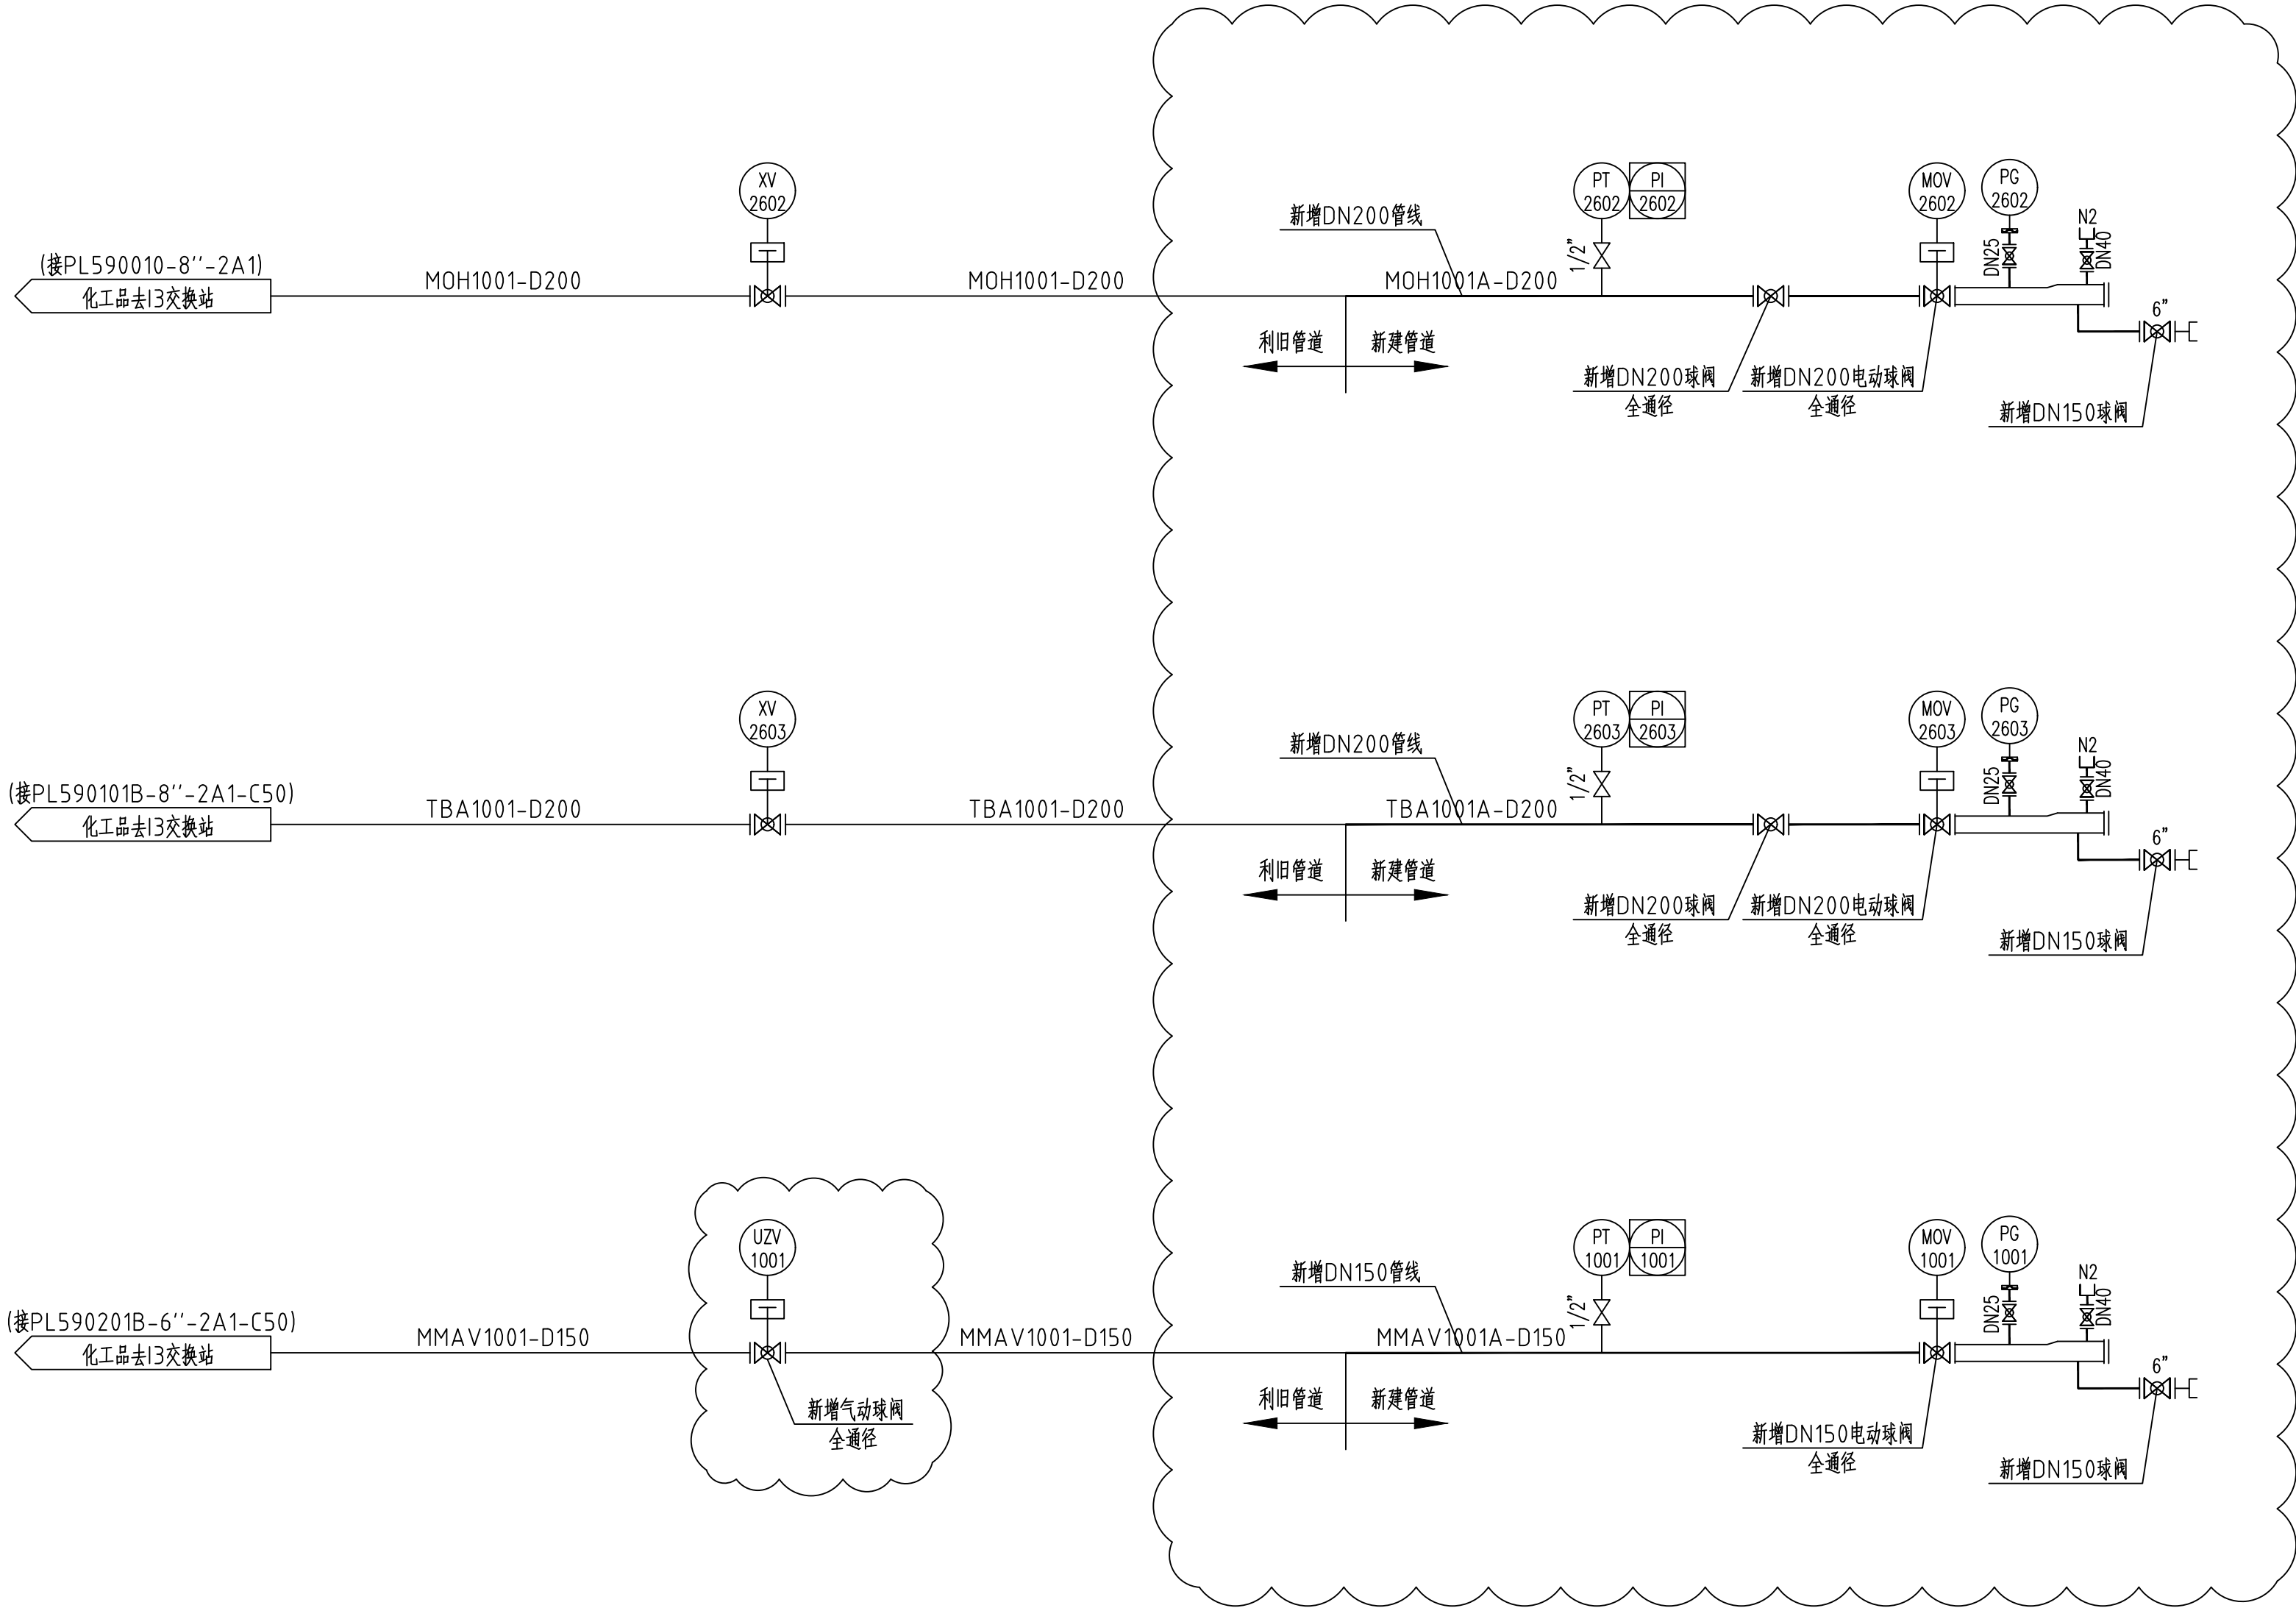

注：云线部分为本次改造流程，其余均为现状流程。

工程勘察资质(出图)专用章
安徽华东化工医药工程有限责任公司
化工石化医药行业甲级 证书编号: A134008172
中华人民共和国住房和城乡建设部监制
有效期至 2029年09月20日

版次	REV	说明	设计	校核	审核	批准	日期
REV		DESCRIPTION	PRE'D	CHKD	APPR	AUTH'D	DATE
华东工程 安徽华东化工医药工程有限责任公司							
ANHUI HUADONG CHEMICAL AND MEDICAL ENGINEERING CO., LTD							
本图纸版权为安徽华东化工医药工程有限责任公司所有, 未经本公司许可不得转让或复制给第三方。 The copyright of this drawing is the property of ANHUI HUADONG CHEMICAL AND MEDICAL ENGINEERING CO., LTD. Unauthorized disclosure or duplication to the third party is not permitted.							
业主	江苏威达建设集团有限公司			图名	工艺及仪表流程图一		
项目	欧德优创(惠州)仓储有限责任公司管线改造项目			DRAWING NAME			
装置/工区	欧德优创码头管线改造项目			项目号	N26002		
设计阶段	详细设计	专业	储运	比例	图号	N26002D02ST01DW01	
DESIGN STAGE		SPEC	SCALE	---	DRAWING NO.		